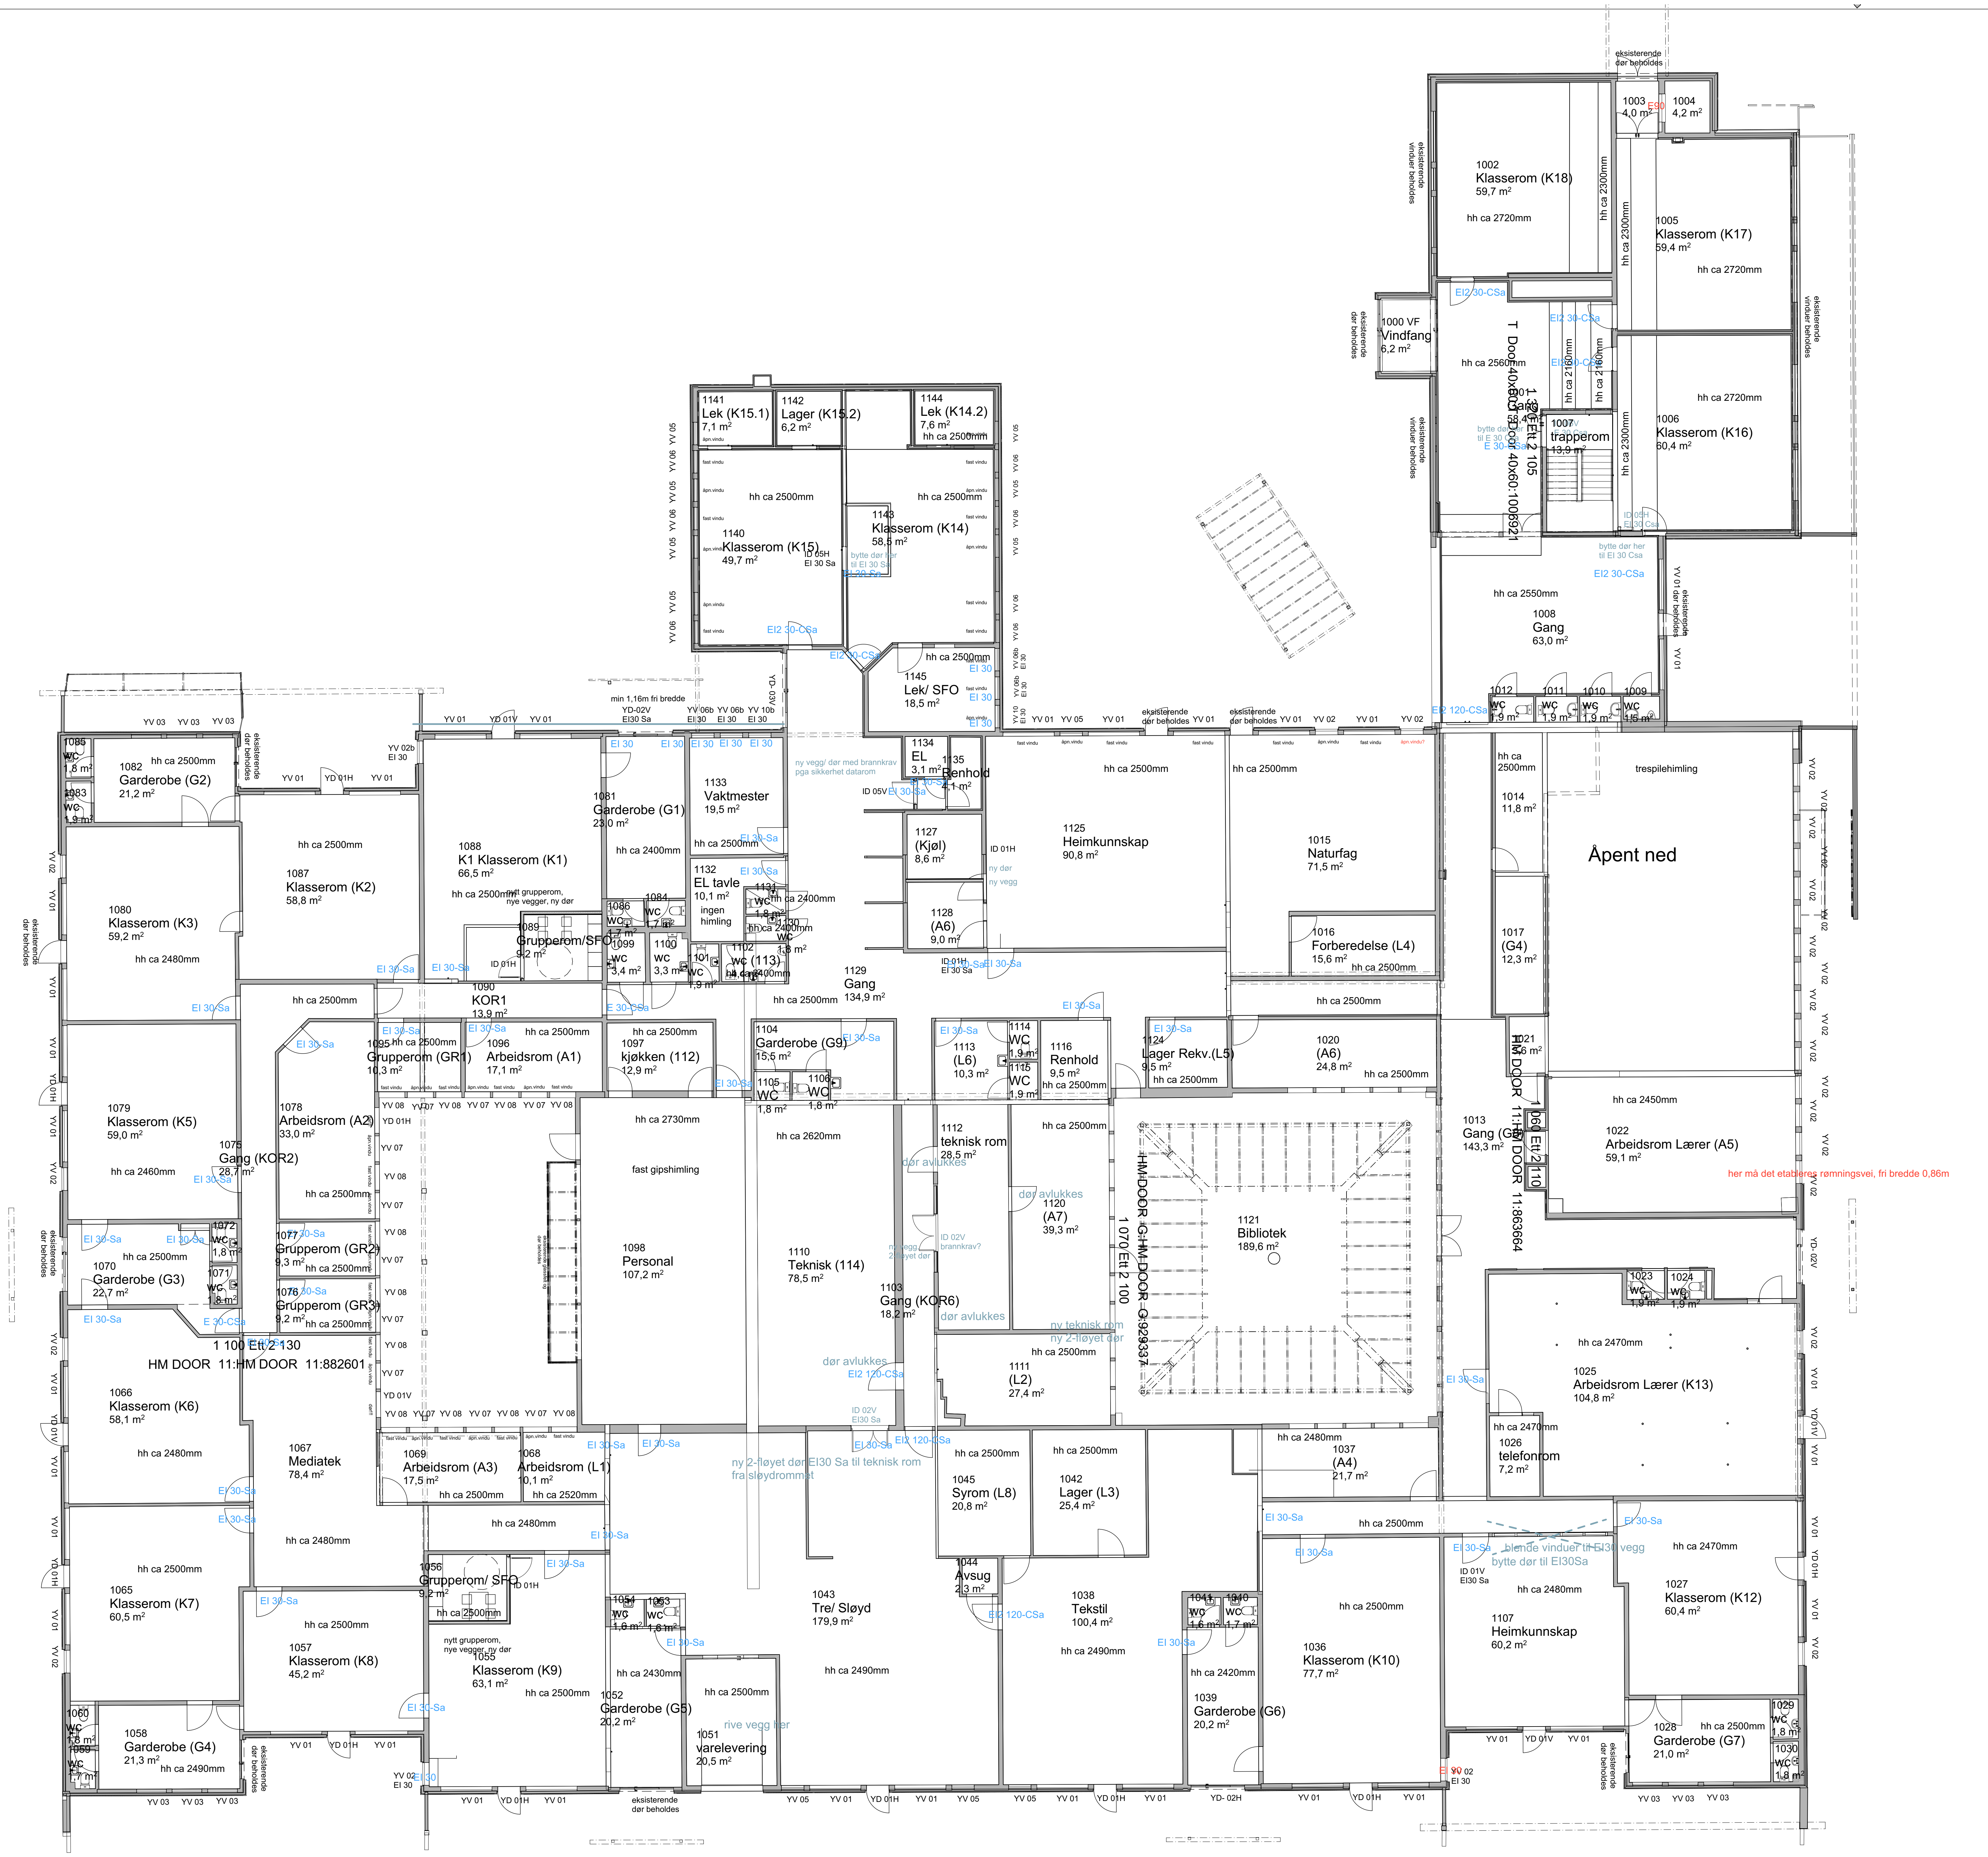
1002 Klasserom (K18) 59,7 m²
1003 4,0 m²
1004 4,2 m²
1005 Klasserom (K17) 59,4 m²
1000 VF Vindfang 6,2 m²
1006 Klasserom (K16) 60,4 m²
1007 trapperom 13,9 m²
1008 Gang 63,0 m²
1009 WC 1,8 m²
1010 WC 1,9 m²
1011 WC 1,9 m²
1012 WC 1,9 m²
1141 Lek (K15.1) 7,1 m²
1142 Lager (K15.2) 6,2 m²
1144 Lek (K14.2) 7,6 m²
1140 Klasserom (K15) 49,7 m²
1143 Klasserom (K14) 58,5 m²
1145 Lek/ SFO 18,5 m²
1085 WC 1,8 m²
1083 WC 1,9 m²
1082 Garderobe (G2) 21,2 m²
1080 Klasserom (K3) 59,2 m²
1087 Klasserom (K2) 58,8 m²
1088 K1 Klasserom (K1) 66,5 m²
1081 Garderobe (G1) 23,0 m²
1133 Vaktmester 19,5 m²
1134 EL 3,1 m²
1135 Renhold 4,1 m²
1125 Heimkunnskap 90,8 m²
1015 Naturfag 71,5 m²
1014 11,8 m²
Åpent ned
1127 (Kjøl) 8,6 m²
1128 (A6) 9,0 m²
1132 EL tavle 10,1 m²
1089 Grupperom/SFO 9,2 m²
1090 KOR1 13,9 m²
1129 Gang 134,9 m²
1016 Forberedelse (L4) 15,6 m²
1017 (G4) 12,3 m²
1079 Klasserom (K5) 59,0 m²
1078 Arbeidsrom (A2) 33,0 m²
1095 Grupperom (GR1) 10,3 m²
1096 Arbeidsrom (A1) 17,1 m²
1097 kjøkken (112) 12,9 m²
1104 Garderobe (G9) 15,6 m²
1113 (L6) 10,3 m²
1116 Renhold 9,5 m²
1124 Lager Rekv.(L5) 9,5 m²
1020 (A6) 24,8 m²
1022 Arbeidsrom Lærer (A5) 59,1 m²
1013 Gang (G8) 143,3 m²
1075 Gang (KOR2) 28,7 m²
1098 Personal 107,2 m²
1110 Teknisk (114) 78,5 m²
1112 teknisk rom 28,5 m²
1120 (A7) 39,3 m²
1121 Bibliotek 189,6 m²
1103 Gang (KOR6) 18,2 m²
1111 (L2) 27,4 m²
1070 Garderobe (G3) 22,7 m²
1077 Grupperom (GR2) 9,3 m²
1076 Grupperom (GR3) 9,2 m²
1066 Klasserom (K6) 58,1 m²
1067 Mediatek 78,4 m²
1069 Arbeidsrom (A3) 17,5 m²
1068 Arbeidsrom (L1) 10,1 m²
1045 Syrom (L8) 20,8 m²
1042 Lager (L3) 25,4 m²
1037 (A4) 21,7 m²
1025 Arbeidsrom Lærer (K13) 104,8 m²
1026 telefonrom 7,2 m²
1023 WC 1,9 m²
1024 WC 1,9 m²
1065 Klasserom (K7) 60,5 m²
1057 Klasserom (K8) 45,2 m²
1056 Grupperom/ SFO 9,2 m²
1055 Klasserom (K9) 63,1 m²
1052 Garderobe (G5) 20,2 m²
1051 varelevering 20,5 m²
1043 Tre/ Sløyd 179,9 m²
1044 Avsug 2,3 m²
1038 Tekstil 100,4 m²
1039 Garderobe (G6) 20,2 m²
1036 Klasserom (K10) 77,7 m²
1107 Heimkunnskap 60,2 m²
1027 Klasserom (K12) 60,4 m²
1028 Garderobe (G7) 21,0 m²
1029 WC 1,8 m²
1030 WC 1,8 m²
1058 Garderobe (G4) 21,3 m²
1060 WC 1,6 m²
1059 WC 1,7 m²
eksisterende dør beholdes
eksisterende vinduer beholdes
her må det etableres rømningsvei, fri bredde 0,86m
ny 2-fløyet dør EI30 Sa til teknisk rom fra sløydrommet
blende vinduer til EI30 vegg
bytte dør til EI30Sa
rive vegg her
dør avlukkes
ny teknisk rom
ny 2-fløyet dør
trespilehimling
fast gipshimling
HM DOOR 11:HM DOOR 11:882601

RevID	EndrID	Change Name	Dato

Fase
Detaljprosjekt

Revisjon

Status

Lokaliseringsfigur

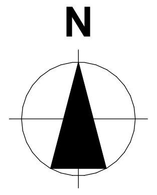

LINK Arkitektur

Tiltakshaver
Sola Kommune

Prosjekt
Dysjaland skole Detaljprosjekt

Tjeltaveien 1
4054 Tjelta

Kontroll prosjekt.

Godkjent	Kontrollert

Ansvarlig
HØE

Dato
Dato oppr.

Prosjektnummer:
16201782

Målestokk
1:200

foreløpig

Tegningsnummer:
A22-102

Tegningstype:
Planer 1:200

Tegningsnavn:
Plan 1.etasje

04.05.2026